


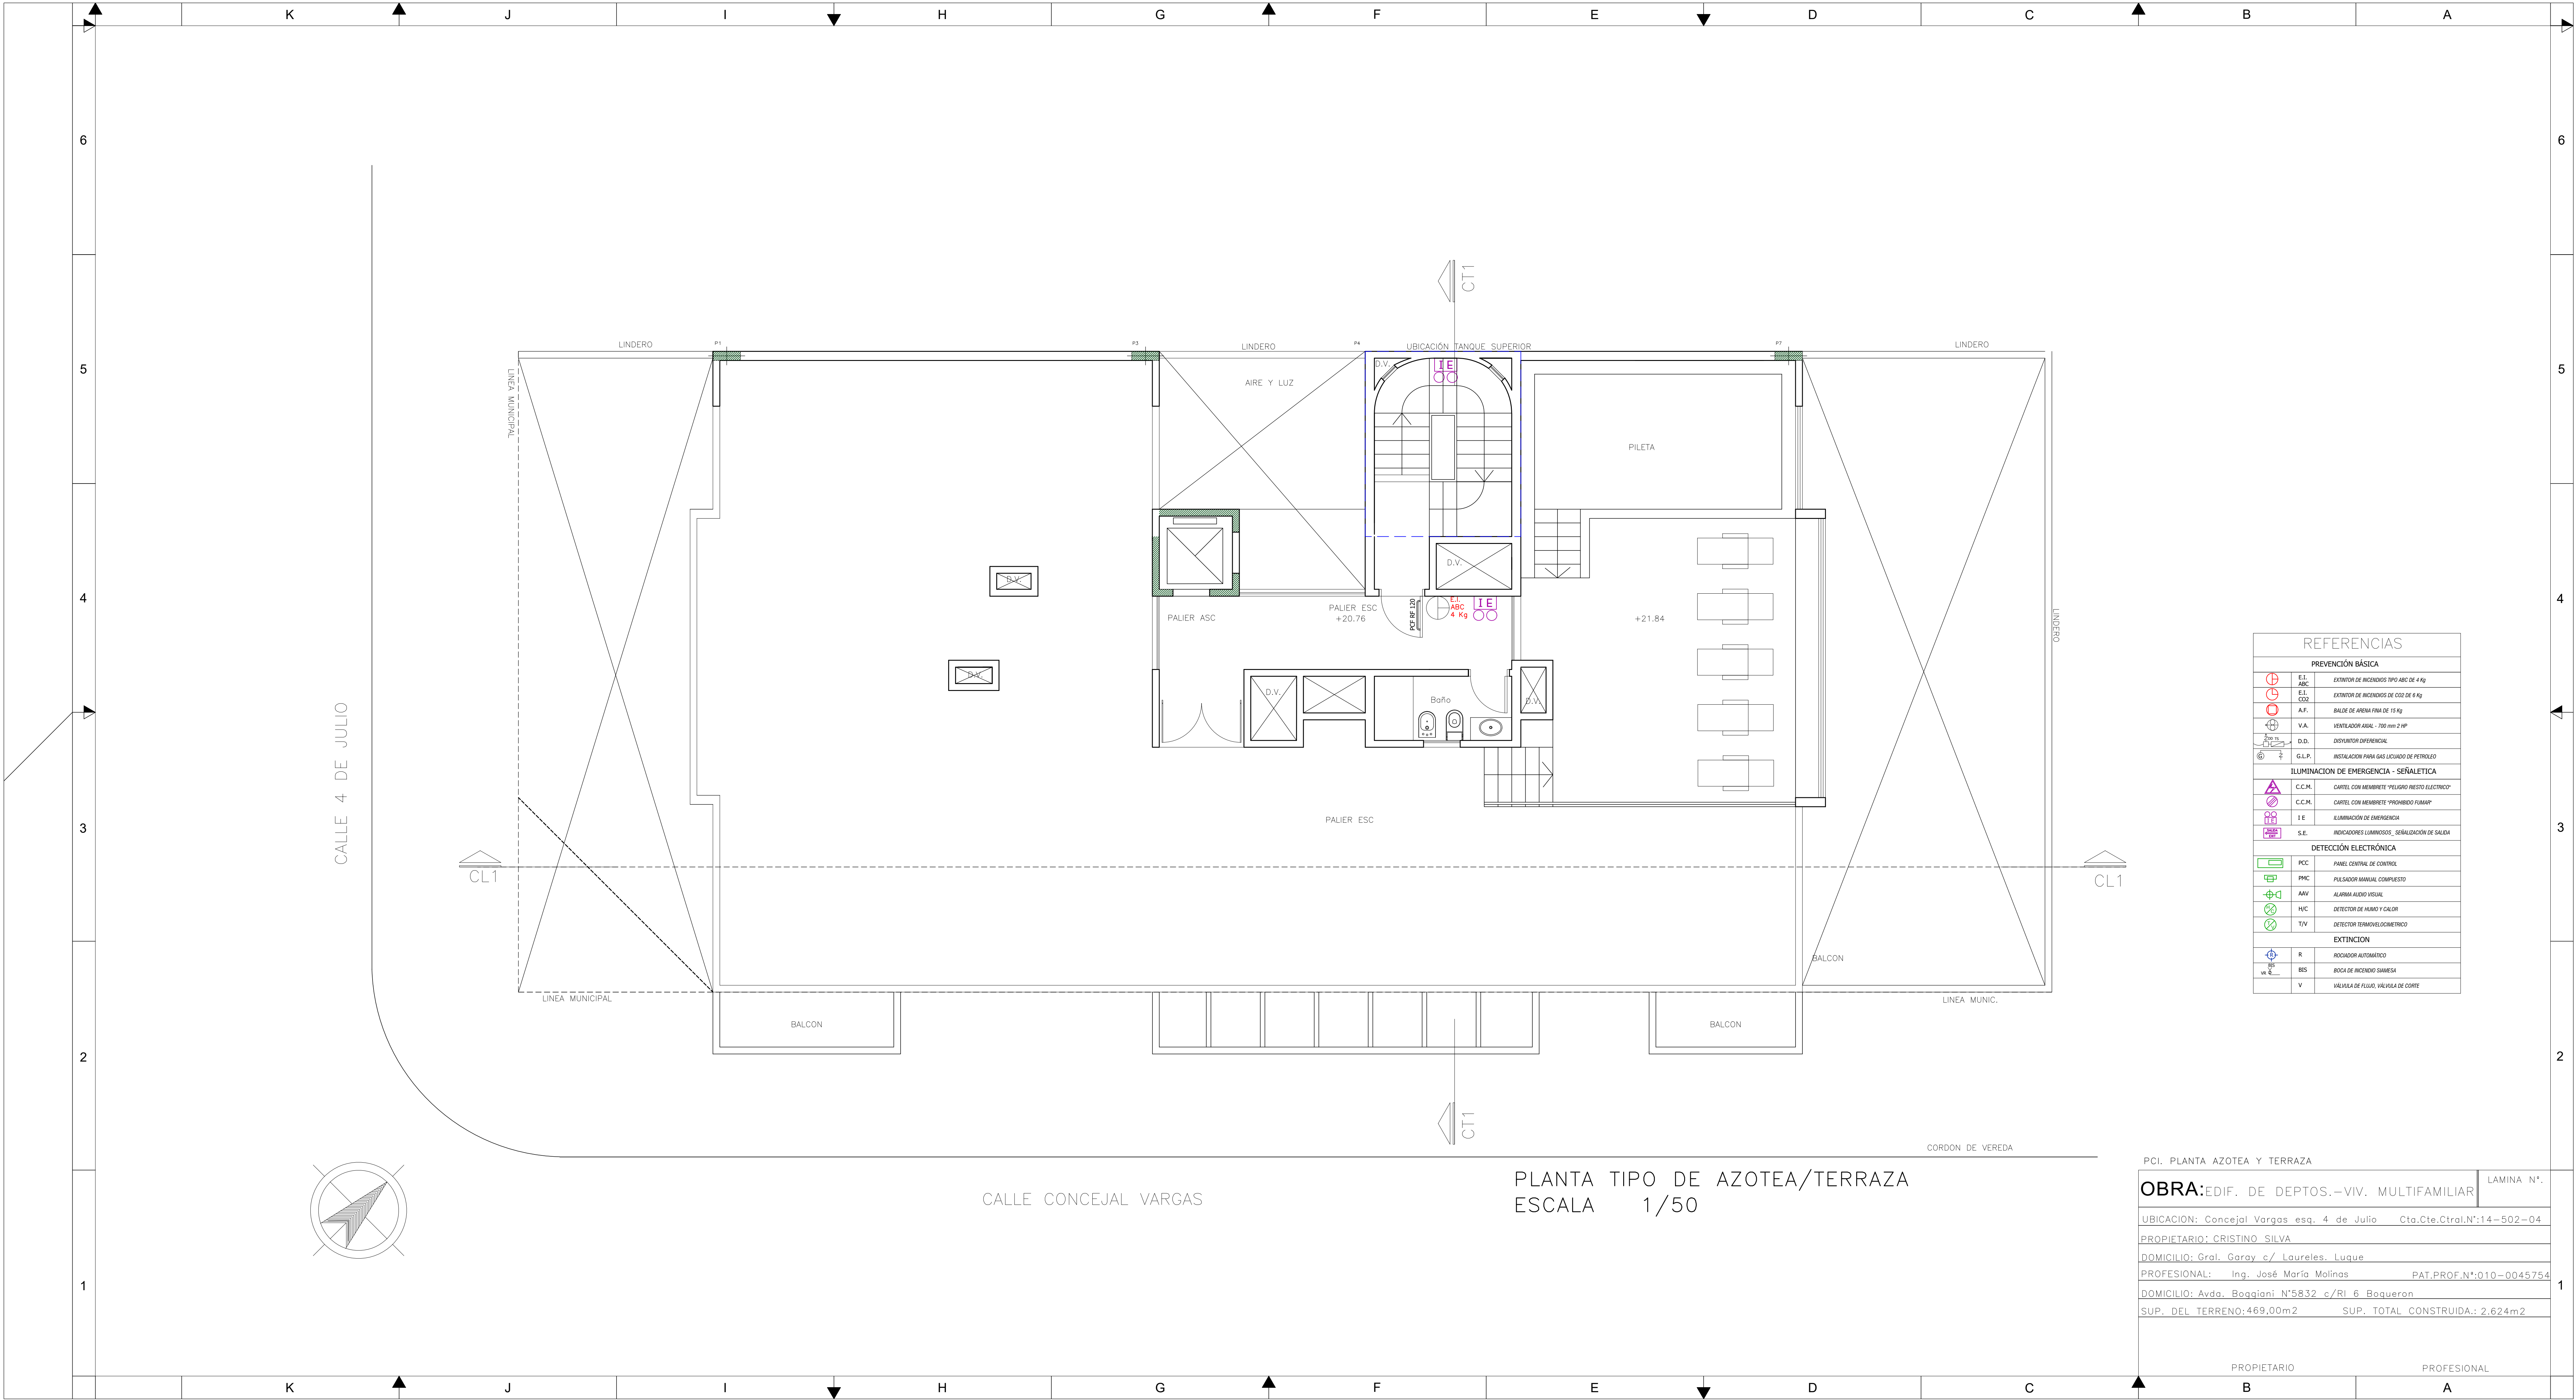

REFERENCIAS	
PREVENCIÓN BÁSICA	
	E.I. INC. EXTINTOR DE INCENDIOS 1000 ABC DE 4 Kg
	E.I. CO2. EXTINTOR DE INCENDIOS DE CO2 DE 8 Kg
	A.P. BALDE DE AGUA PARA DE 10 Kg
	V.A. VENTILADOR AEREO - 700 mm 2 HP
	D.D. DETECTOR DIFERENCIAL
	S.L.P. INSTALACION PARA GAS LIQUIDO DE PETROLEO
ILUMINACIÓN DE EMERGENCIA - SEÑALÉTICA	
	C.C.M. CARTEL CON ALUMENENTE "PULSADO NUESTRO ELECTRIC"
	C.C.M. CARTEL CON ALUMENENTE "PULSADO FUMAR"
	T.E. ILUMINACION DE EMERGENCIA
	S.E. INDICADORES LUMINOSOS - SEÑALIZACION DE SALIDA
DETECCIÓN ELECTRÓNICA	
	PCC. PANEL CENTRAL DE CONTROL
	PMK. PULSADOR MANUAL COMPLETO
	AVV. ALARMA AUDIO VISUAL
	HVC. DETECTOR DE HUMO Y CALOR
	TVV. DETECTOR TERMOCALORIMETRICO
EXTINCION	
	R. ROCIADOR AUTOMATICO
	BS. BOCINA DE INCENDIO SIRENA
	V. VALVULA DE FILLO VALVULA DE CORTE

PCI. PLANTA AZOTEA Y TERRAZA	
OBRA:EDIF. DE DEPTOS.-VIV. MULTIFAMILIAR	LAMINA N°.
UBICACION: Concejal Vargas esq. 4 de Julio Cta.Cte.Ctral.N°:14-502-04	
PROPIETARIO: CRISTINO SILVA	
DOMICILIO: Gral. Garay c/ Laureles, Luque	
PROFESIONAL: Ing. José María Molinas	PAT.PROF.N°:010-0045754
DOMICILIO: Ayda, Boggiani N°5832 c/Rl 6 Boqueron	
SUP. DEL TERRENO:469,00m2 SUP. TOTAL CONSTRUIDA.: 2.624m2	
PROPIETARIO PROFESIONAL	