


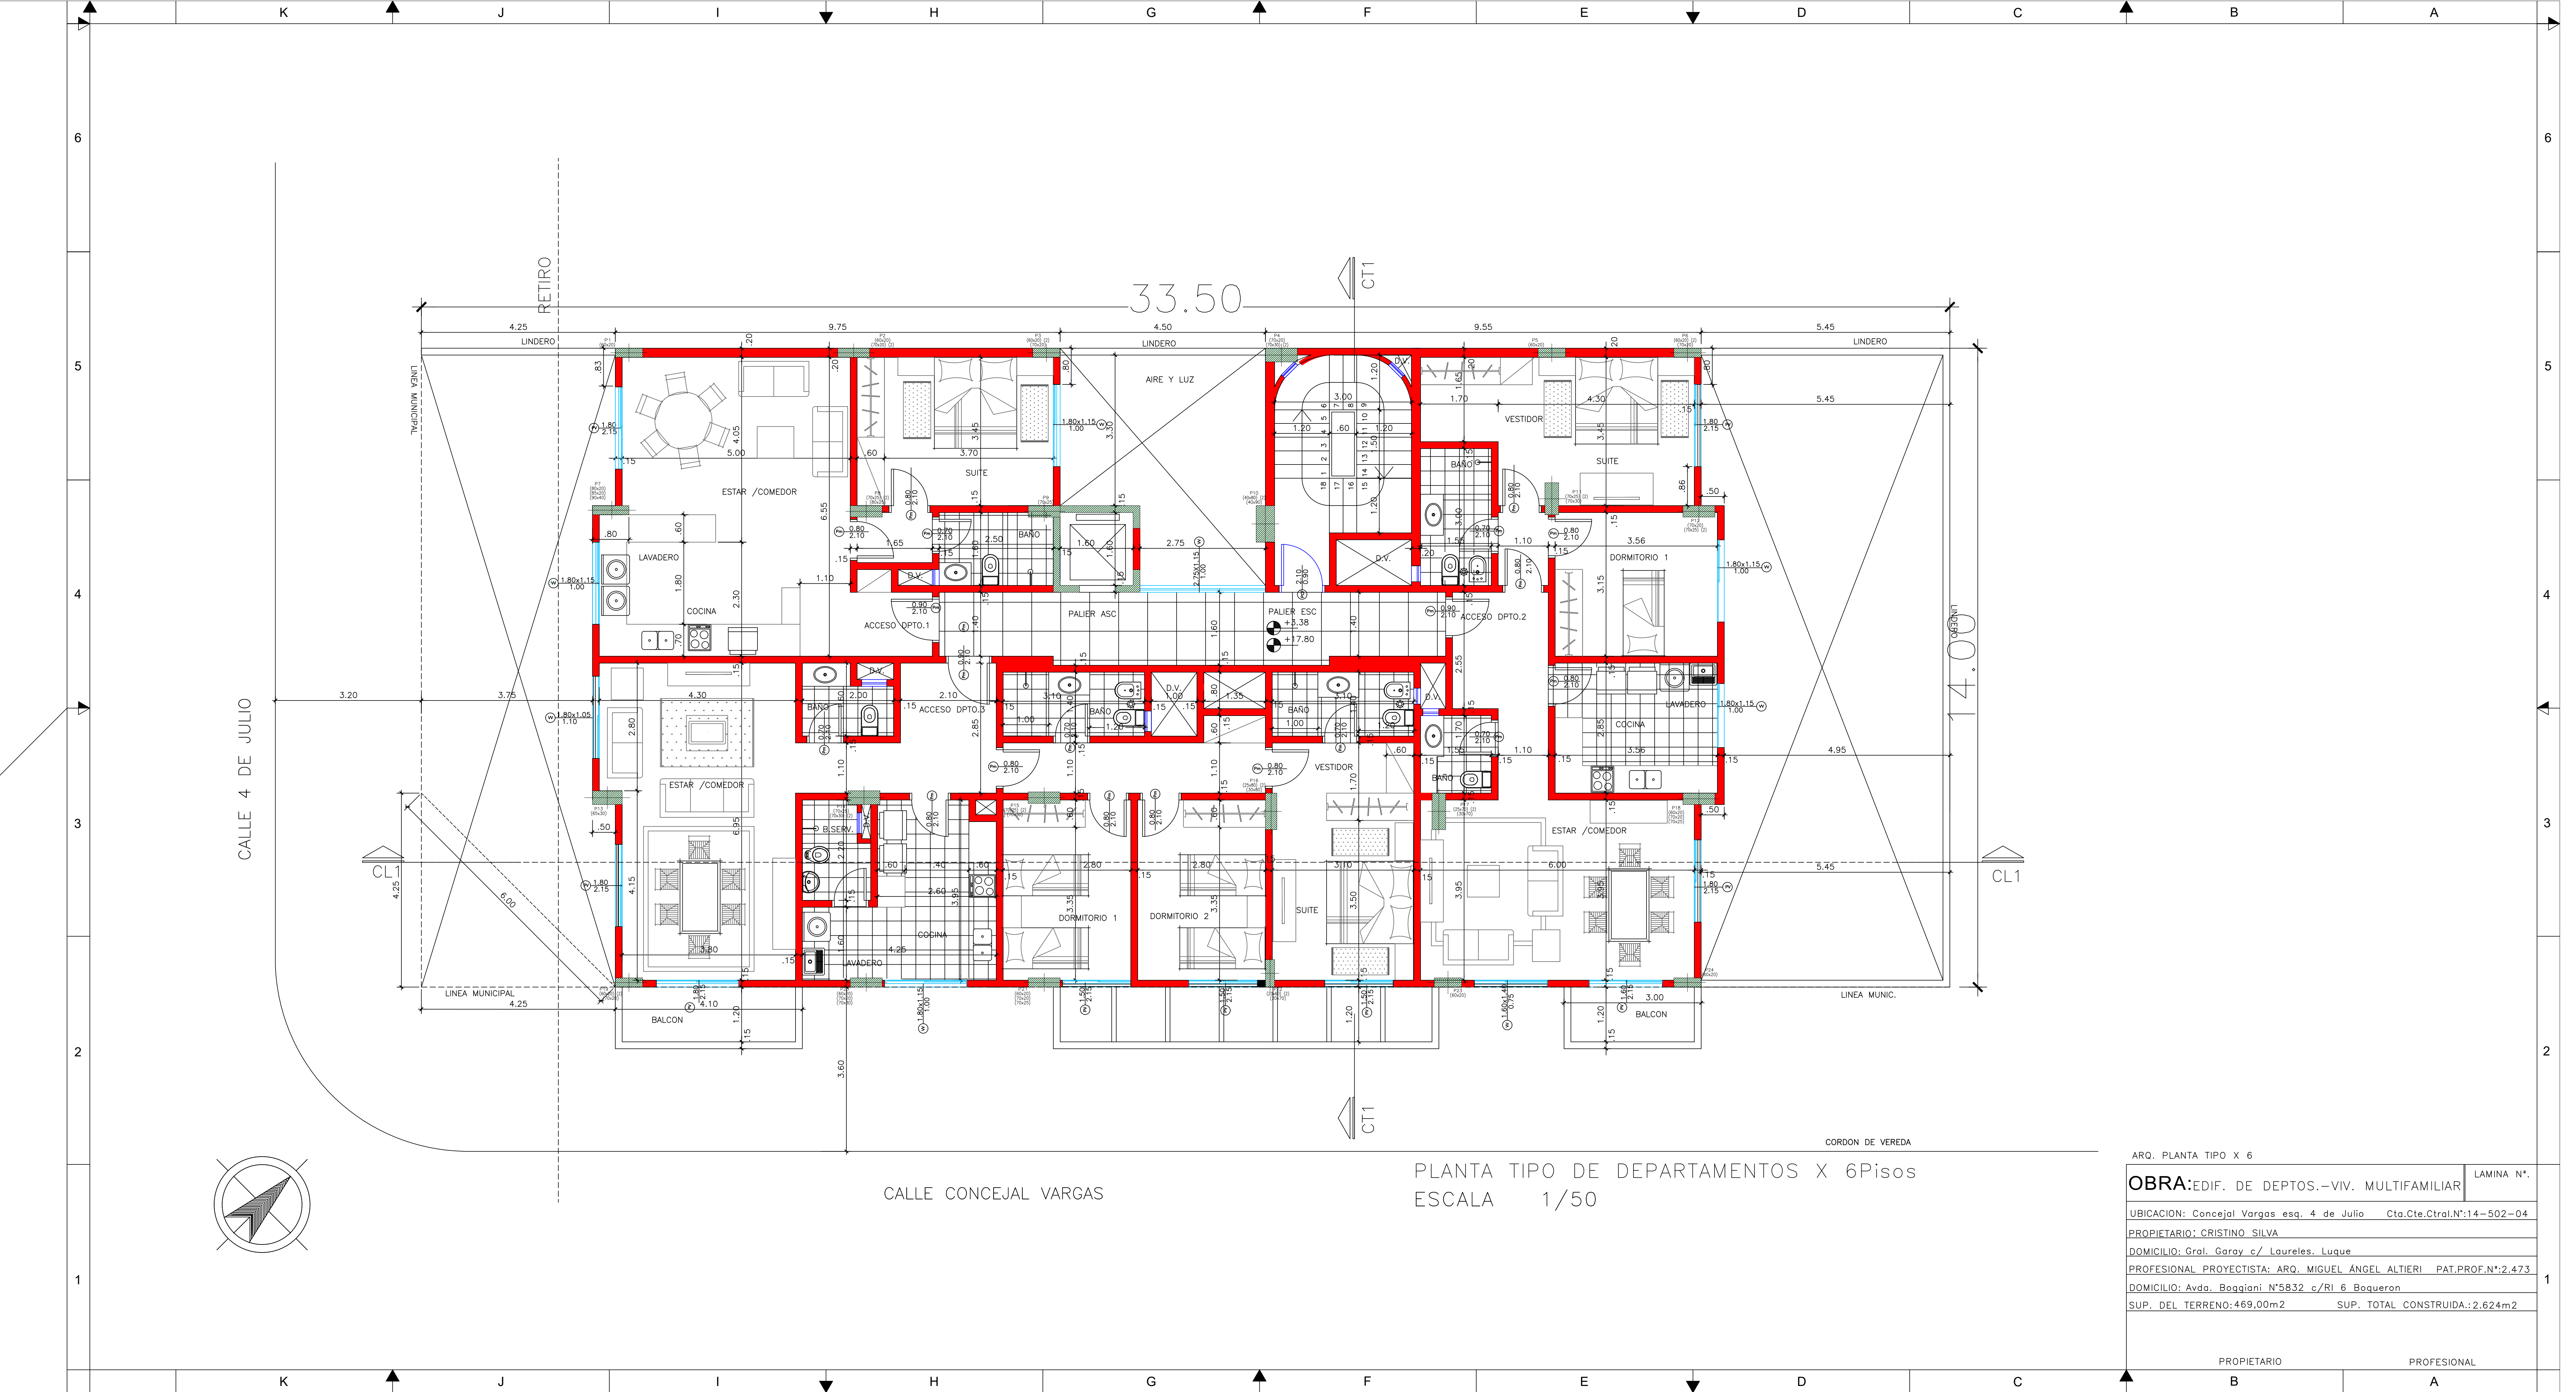

PLANTA TIPO DE DEPARTAMENTOS X 6Pisos  
ESCALA 1/50

|                                                                       |                               |
|-----------------------------------------------------------------------|-------------------------------|
| ARQ. PLANTA TIPO X 6                                                  |                               |
| OBRA:EDIF. DE DEPTOS.-VIV. MULTIFAMILIAR                              | LAMINA N°.                    |
| UBICACION: Concejal Vargas esq. 4 de Julio Cta.Cte.Ctral.N°:14-502-04 |                               |
| PROPIETARIO: CRISTINO SILVA                                           |                               |
| DOMICILIO: Gral. Garay c/ Laureles, Luque                             |                               |
| PROFESIONAL PROYECTISTA: ARQ. MIGUEL ÁNGEL ALTIERI PAT.PROF.N°:2.473  |                               |
| DOMICILIO: Avda. Boqajani N°5832 c/RI 6 Boqueron                      |                               |
| SUP. DEL TERRENO:469,00m2                                             | SUP. TOTAL CONSTRUIDA:2.624m2 |

PROPIETARIO PROFESIONAL

B A