


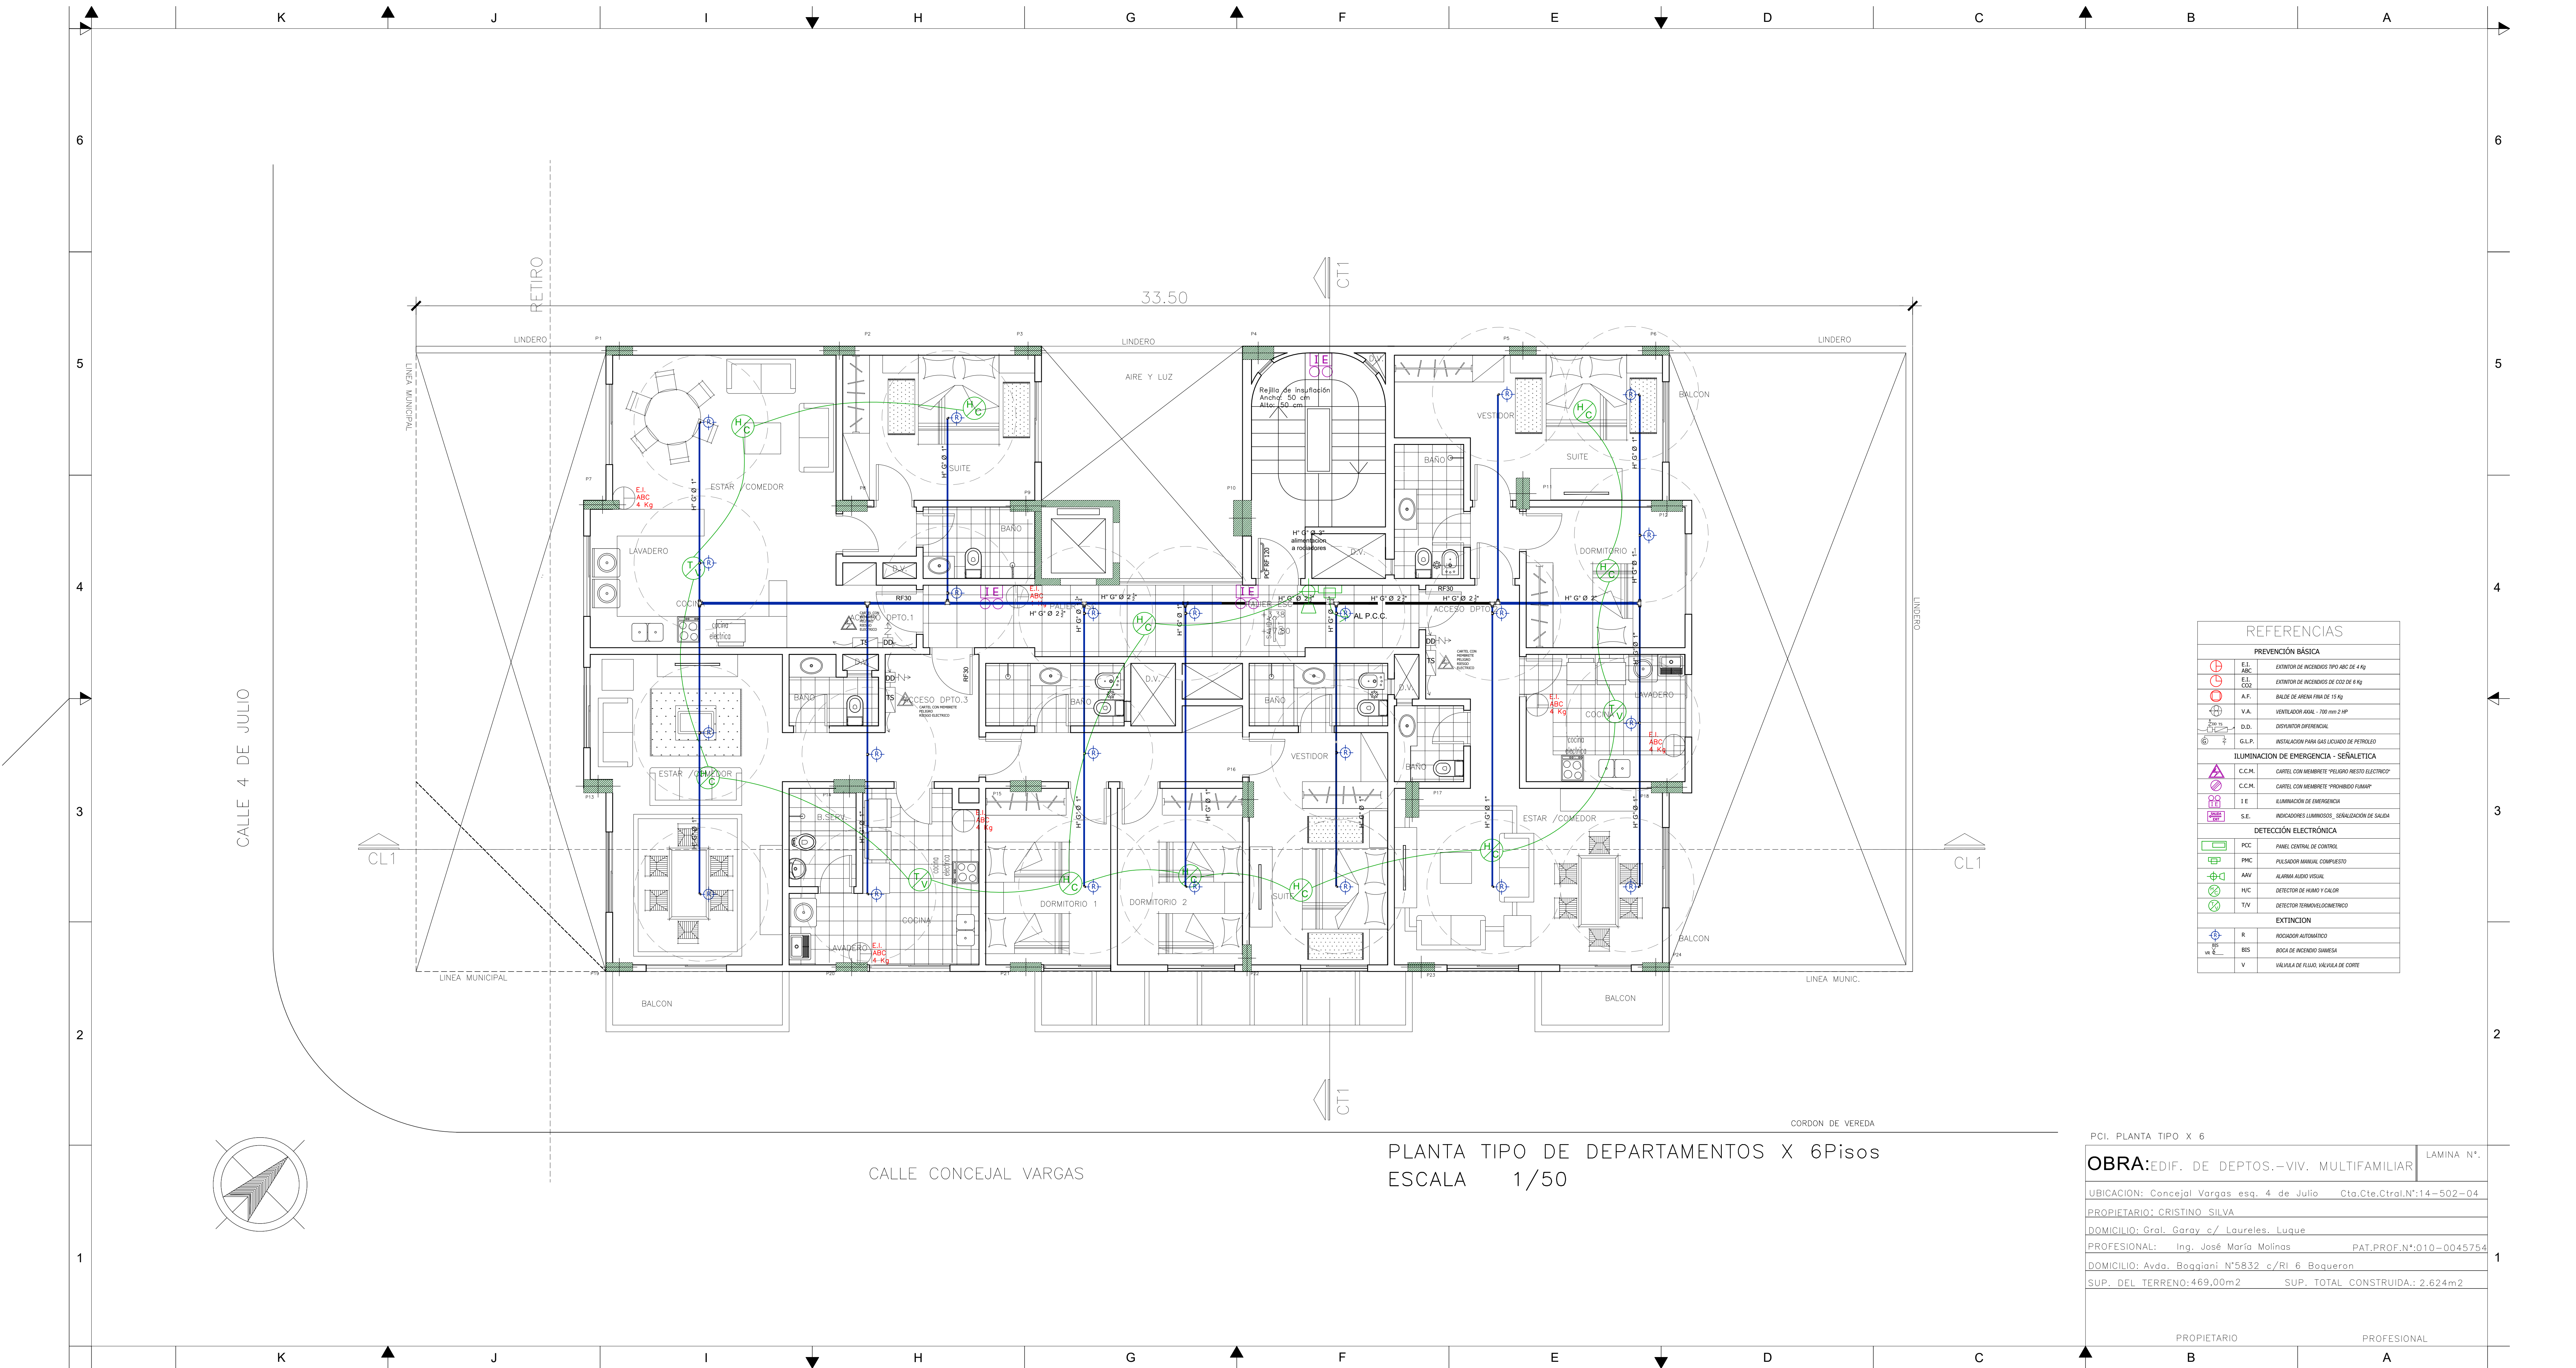

REFERENCIAS	
PREVENCIÓN BÁSICA	
	E.I. ABC EXTINTOR DE INCENDIOS TIPO ABC DE 4 Kg
	E.I. CO2 EXTINTOR DE INCENDIOS DE CO2 DE 4 Kg
	A.F. BALDE DE ARENA PARA DE 15 Kg
	V.A. VENTILADOR ASAL - 700 mm 2 HP
	D.D. DISYUNTOR DIFERENCIAL
	GL.P. INSTALACION PARA GAS LICUADO DE PETROLIO
ILUMINACIÓN DE EMERGENCIA - SEÑALÉTICA	
	C.C.M. CARTEL CON MEMBRANA "PULSADO INSTO ELECTROF"
	C.C.M. CARTEL CON MEMBRANA "PULSADO INSTO FUMAP"
	I.E. ILUMINACIÓN DE EMERGENCIA
	S.E. INDICADORES LUMINOSOS - SEÑALIZACIÓN DE SALIDA
DETECCIÓN ELECTRÓNICA	
	P.C.C. PANEL CENTRAL DE CONTROL
	P.M.C. PULSADOR MANUAL COMPLETO
	A.A.V. ALARMA AUDIO VISUAL
	H.V.C. DETECTOR DE HUMO Y CALOR
	T.V. DETECTOR THERMOELECTRÓNICO
EXTINCIÓN	
	R. RODAMINIO AUTOMÁTICO
	B.B. BOCAL DE INCENDIO SUMERSA
	V. VÁLVULA DE FUGA VÁLVULA DE CORTE

PCI, PLANTA TIPO X 6

OBRA:EDIF. DE DEPTOS.-VIV. MULTIFAMILIAR	LAMINA N°.
UBICACIÓN: Concejal Vargas esq. 4 de Julio Cta.Cta.Ctral.N°:14-502-04	
PROPIETARIO: CRISTINO SILVA	
DOMICILIO: Gral. Garay c/ Laureles, Luque	
PROFESIONAL: Ing. José María Molinas	PAT.PROF.N°:010-0045754
DOMICILIO: Avda. Boggiani N°5832 c/Ri 6 Boqueron	
SUP. DEL TERRENO:469,00m2 SUP. TOTAL CONSTRUIDA: 2.624m2	

PROPIETARIO	PROFESIONAL
B	A