


Abastecimiento de agua desde la red pública Ø 2 1/2 "

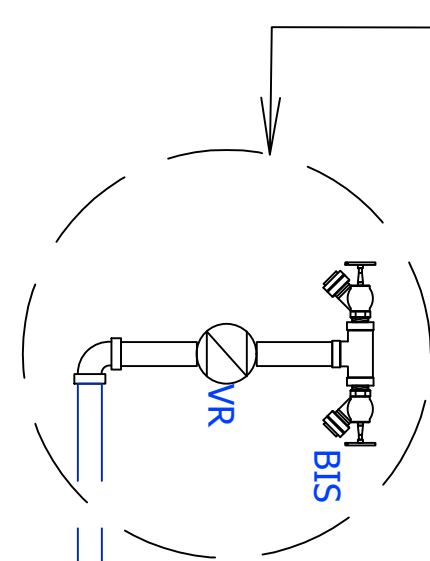


DETALLE PLANTA RESERVORIO PCI ESC 1/20



ELECTROBOMBA PARA ROCIADORES
POTENCIA: 20 HP
FASES: 3
CAUDAL: 60 m3/h
ALTURA DE BOMBEO: 55 m
ELECTROBOMBA TIPO JOCKEY
POTENCIA: 1 HP
FASES: 3
CAUDAL: 20 LITROS/min.
ALTURA DE BOMBEO: 55 m
TANQUE DE HIDROPRESION DE 100 LITROS


AL SISTEMA CONTRA INCENDIO / ROCIADORES 2 1/2"

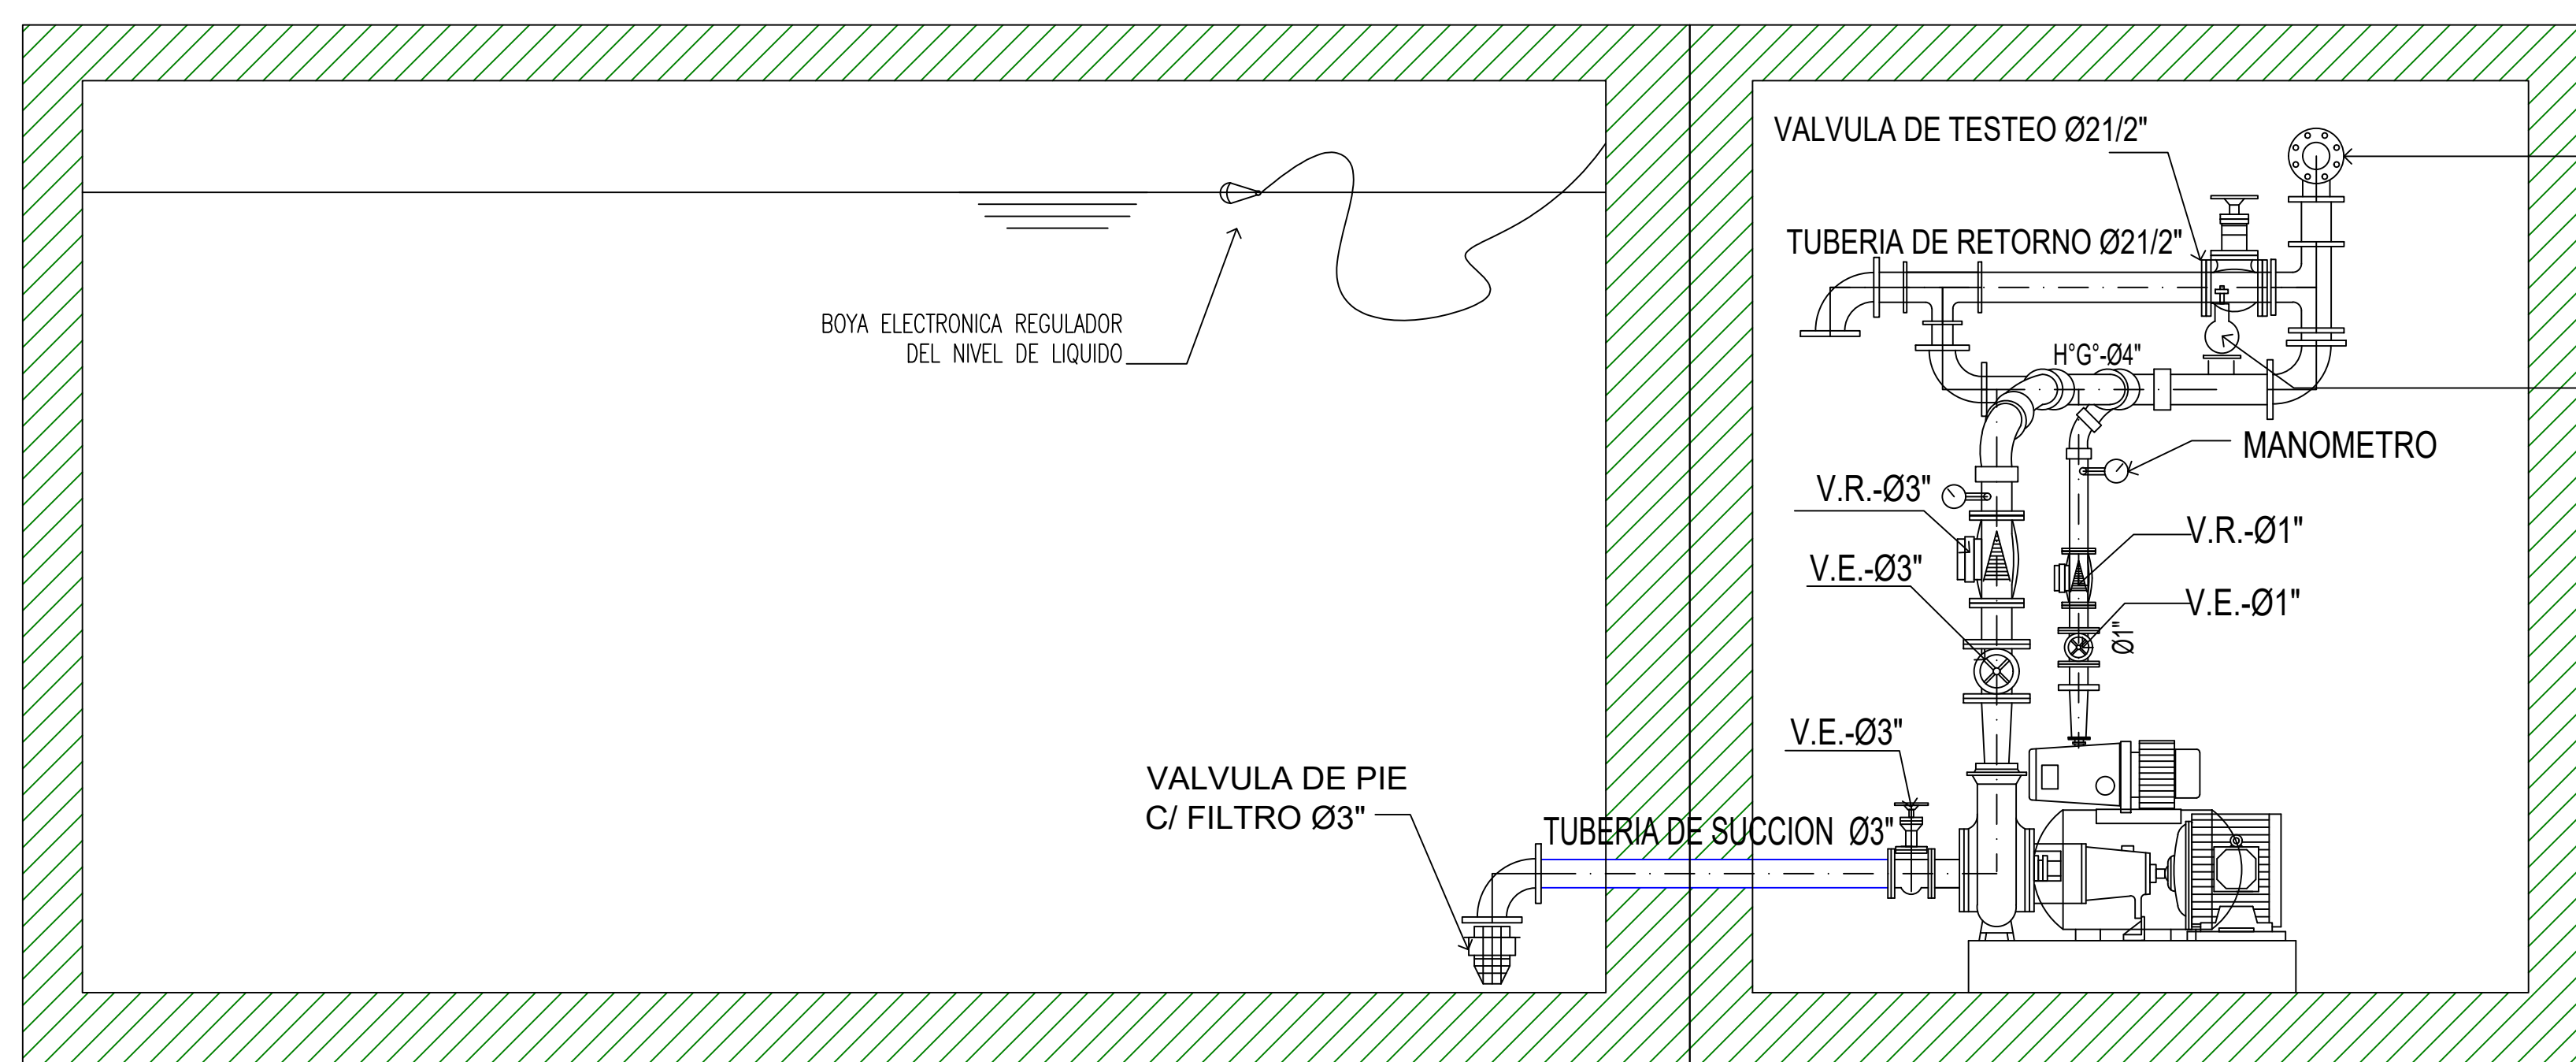


DETALLE CORTE LONGITUDINAL ESC 1/20

AL SISTEMA CONTRA INCENDIO / ROCIADORES Ø3"

VALVULA DE ALIVIO-Ø2"

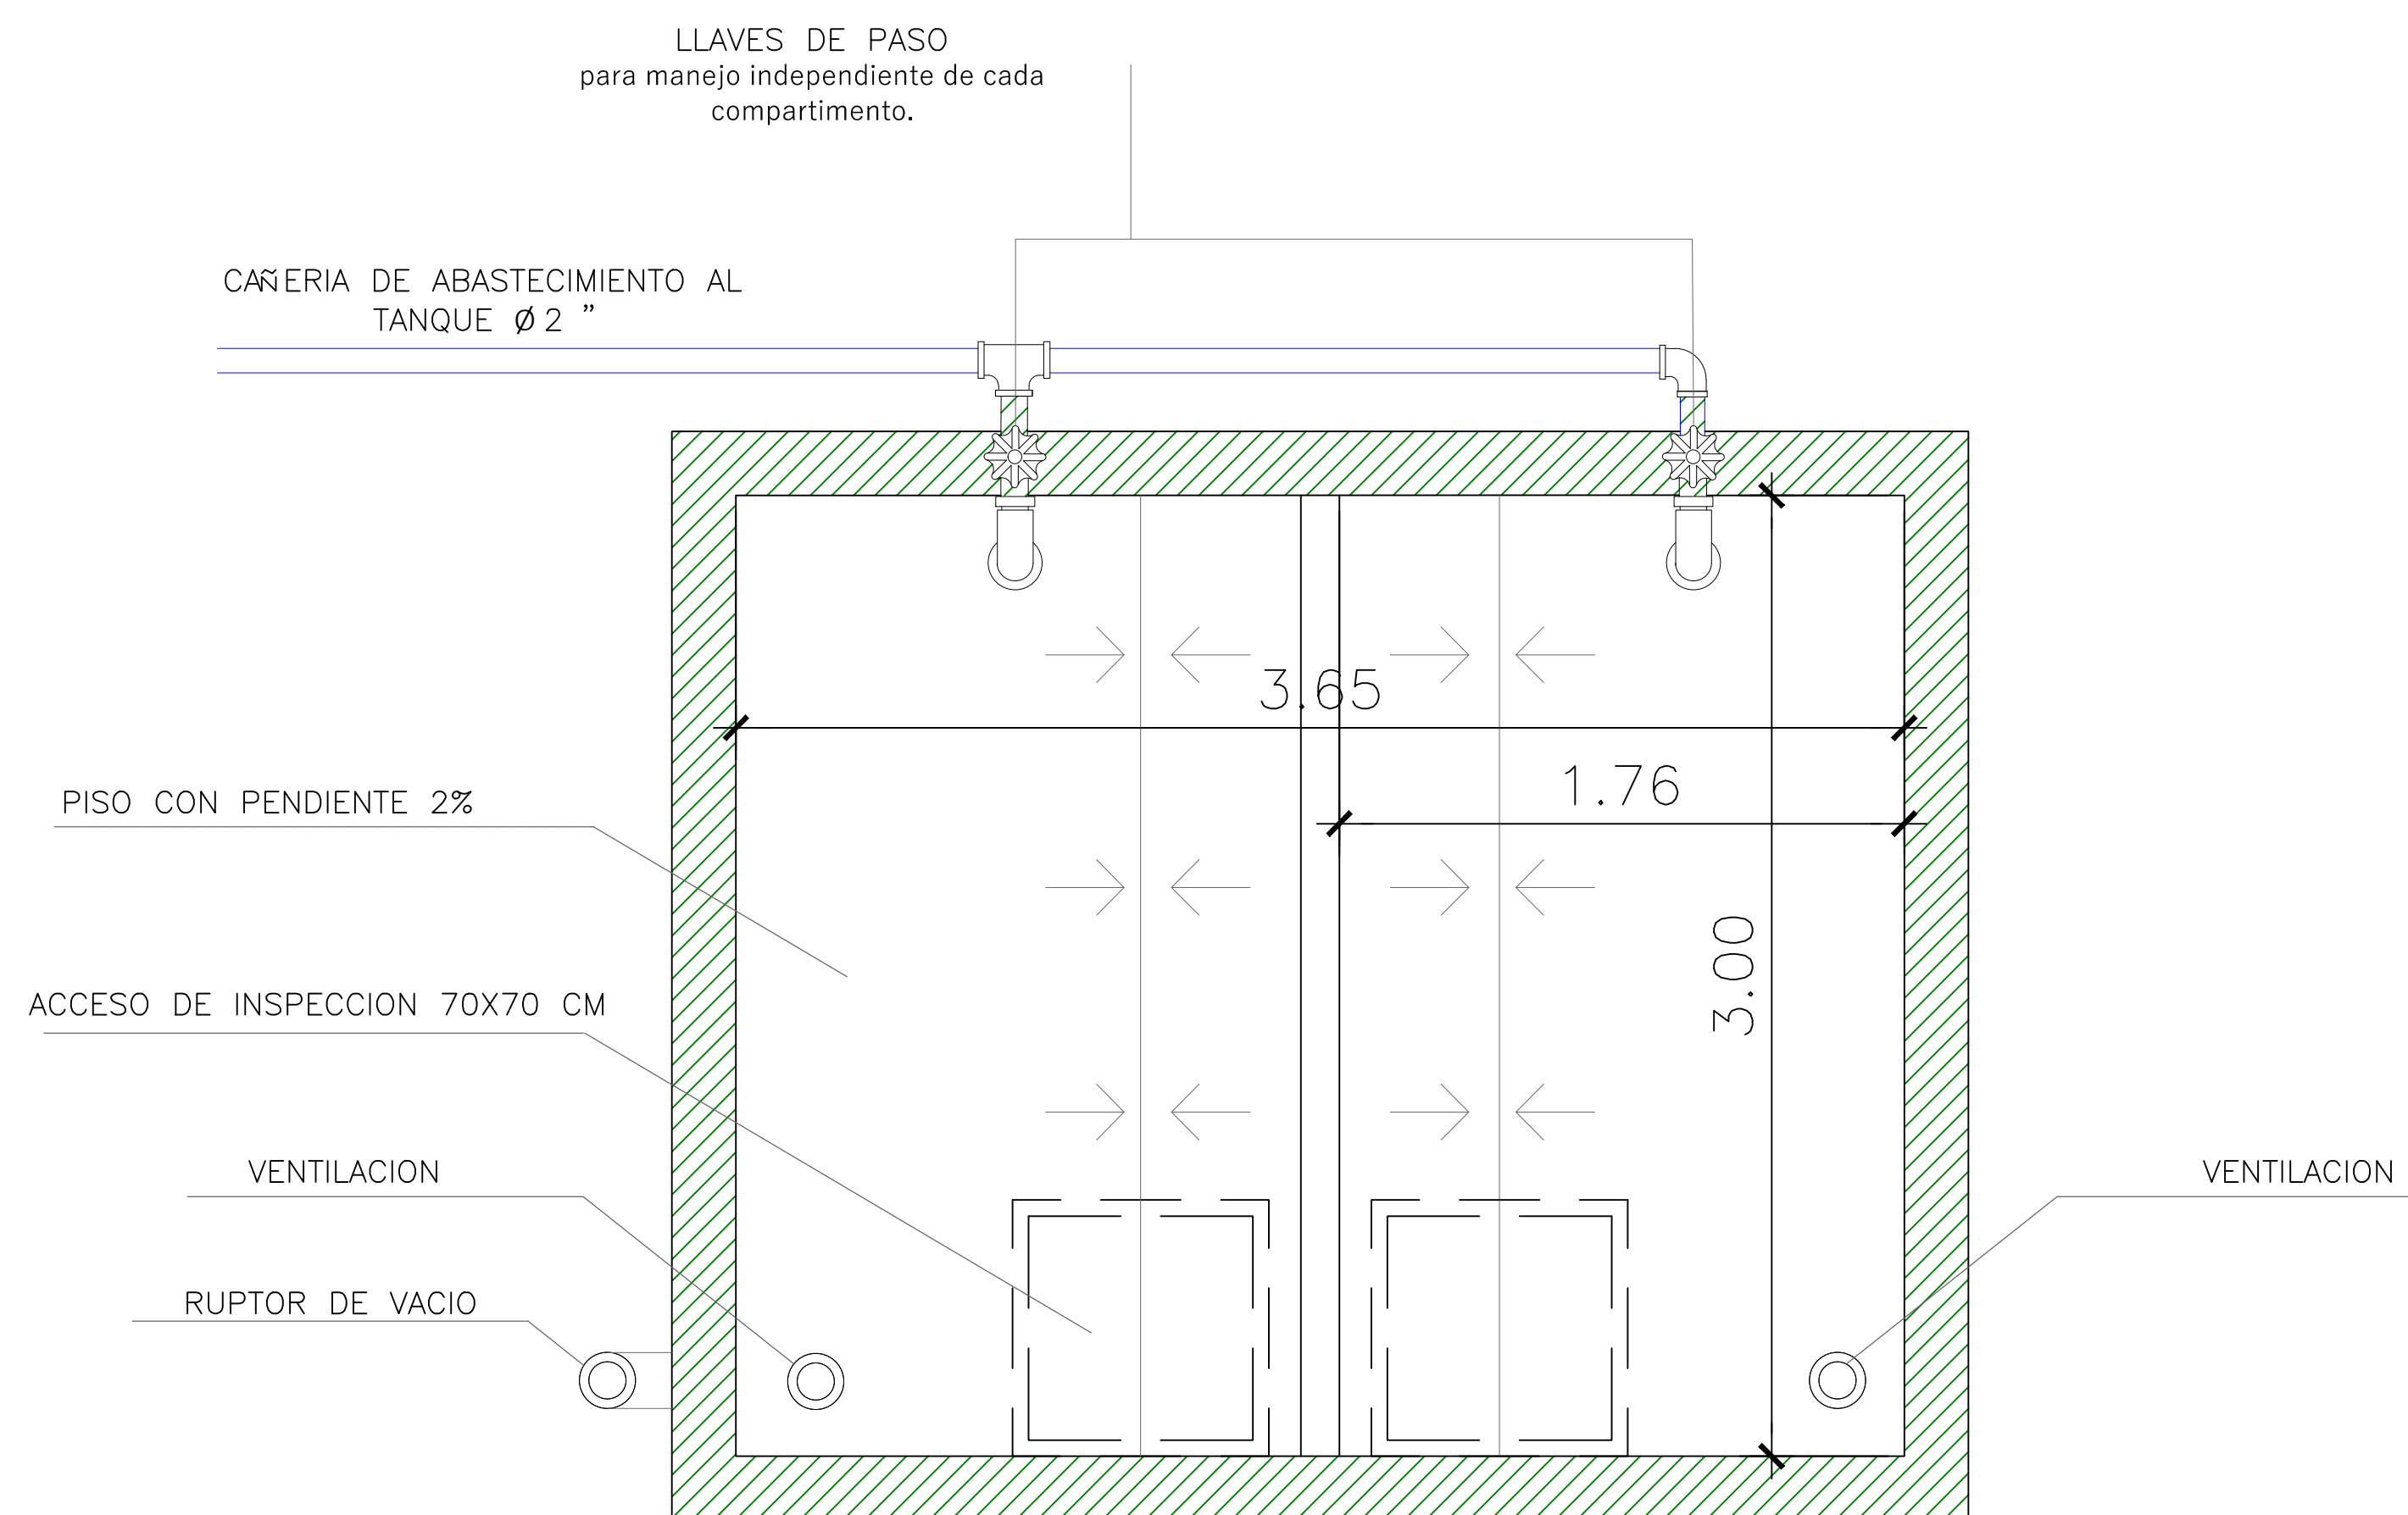

DETALLE TANQUE SUPERIOR ESC 1/20

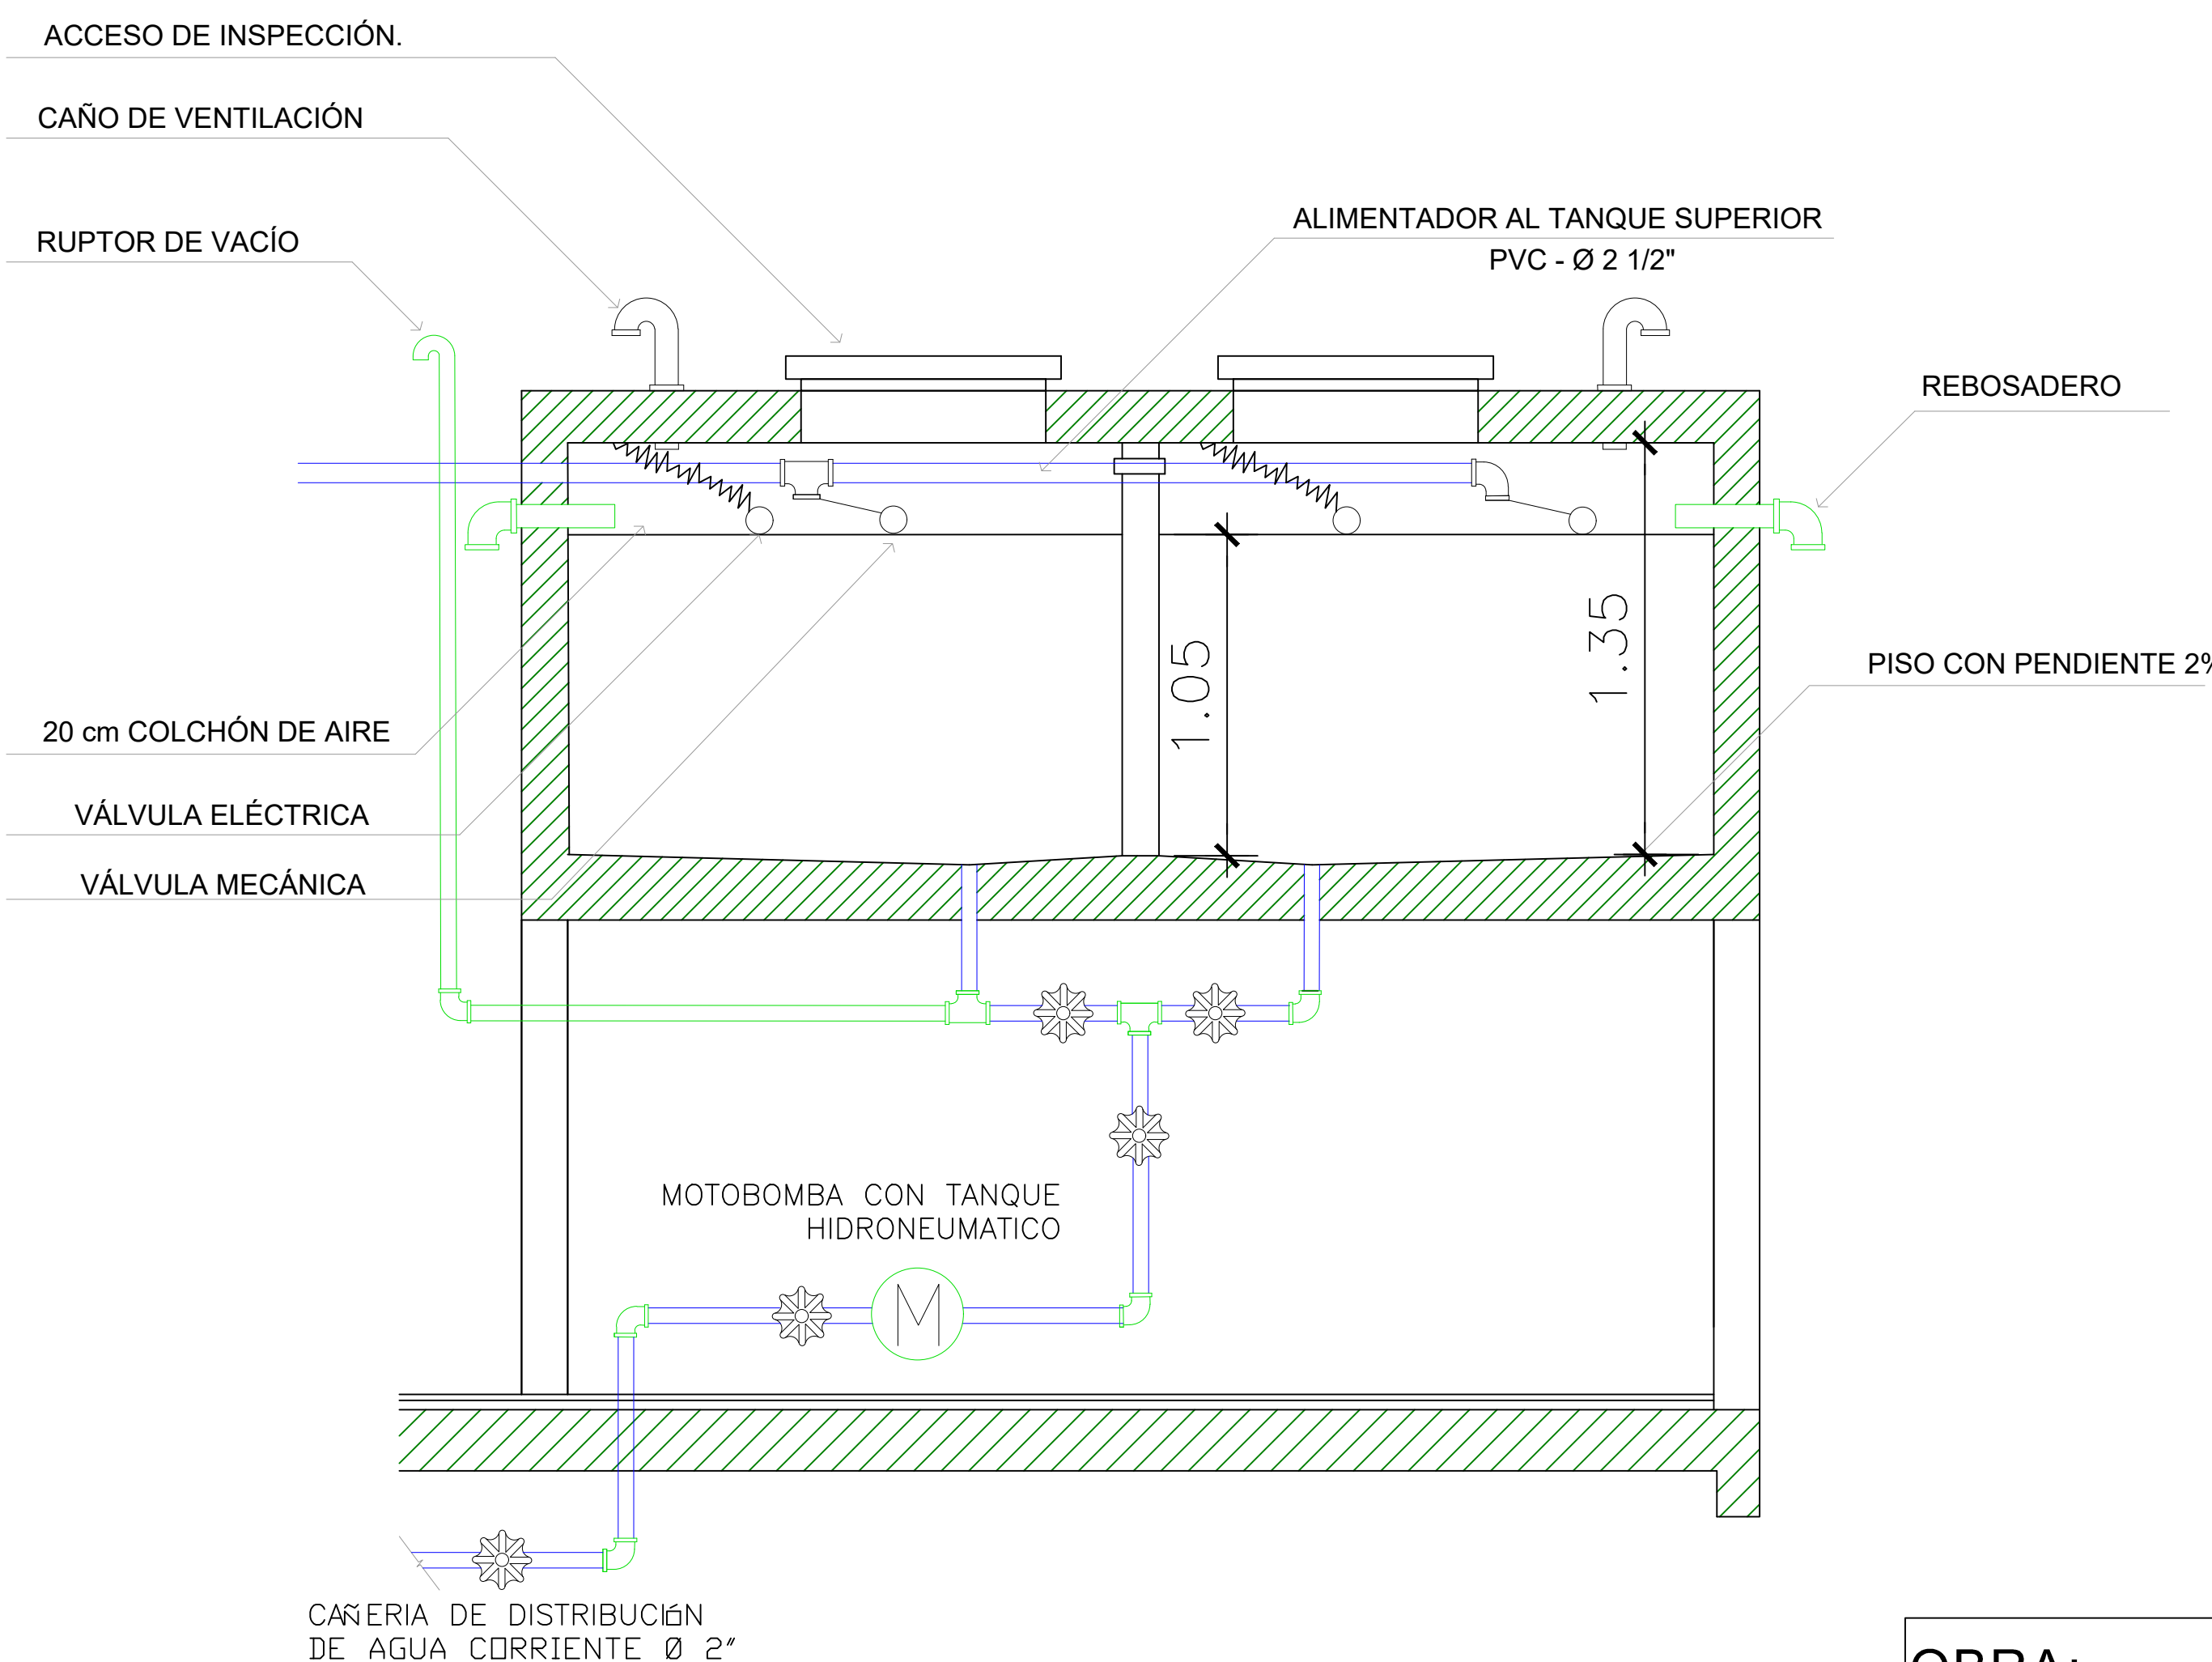

DETALLE CORTE TANQUE SUPERIOR ESC 1/20

OBRA:EDIF. DE DEPTOS.-VIV. MULTIFAMILIAR		LAMINA N°.
UBICACION: Concejal Vargas esq. 4 de Julio Cta.Cte.Ctral:N°14-502-04		
PROPIETARIO: CRISTINO SILVA		
DOMICILIO: Gral. Garay c/ Laureles. Luque		
PROFESIONAL: ING. MOLINAS ROJAS JOSE		PAT.PROF.N°:10-0045754
DOMICILIO: Avda. Boggiani N°5832 c/RI 6 Boqueron		
SUP. DEL TERRENO:469,00m2		SUP. TOTAL CONSTRUIDA.: 2,624m2

PROPIETARIO PROFESIONAL
B A