
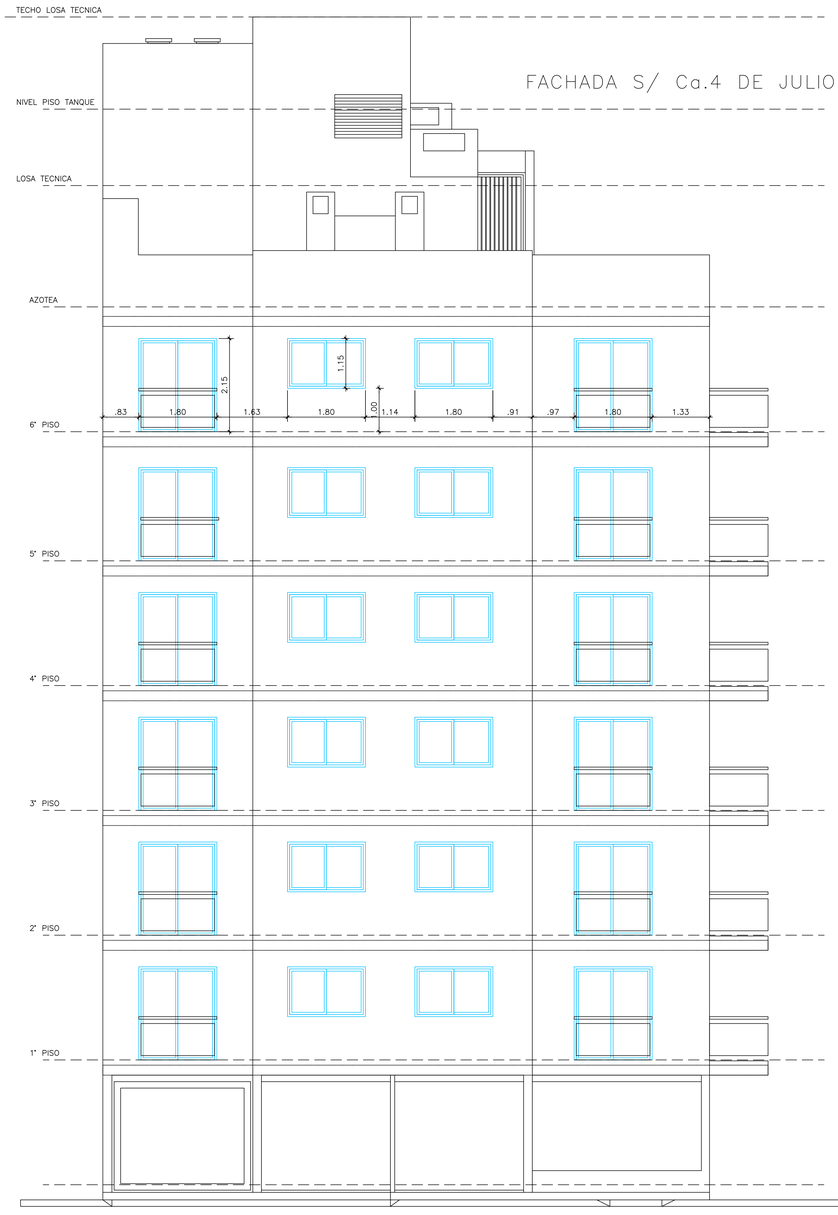



FACHADA S/ Ca.4 DE JULIO

FACHADA S/ Ca.4 DE JULIO
ESC 1/50

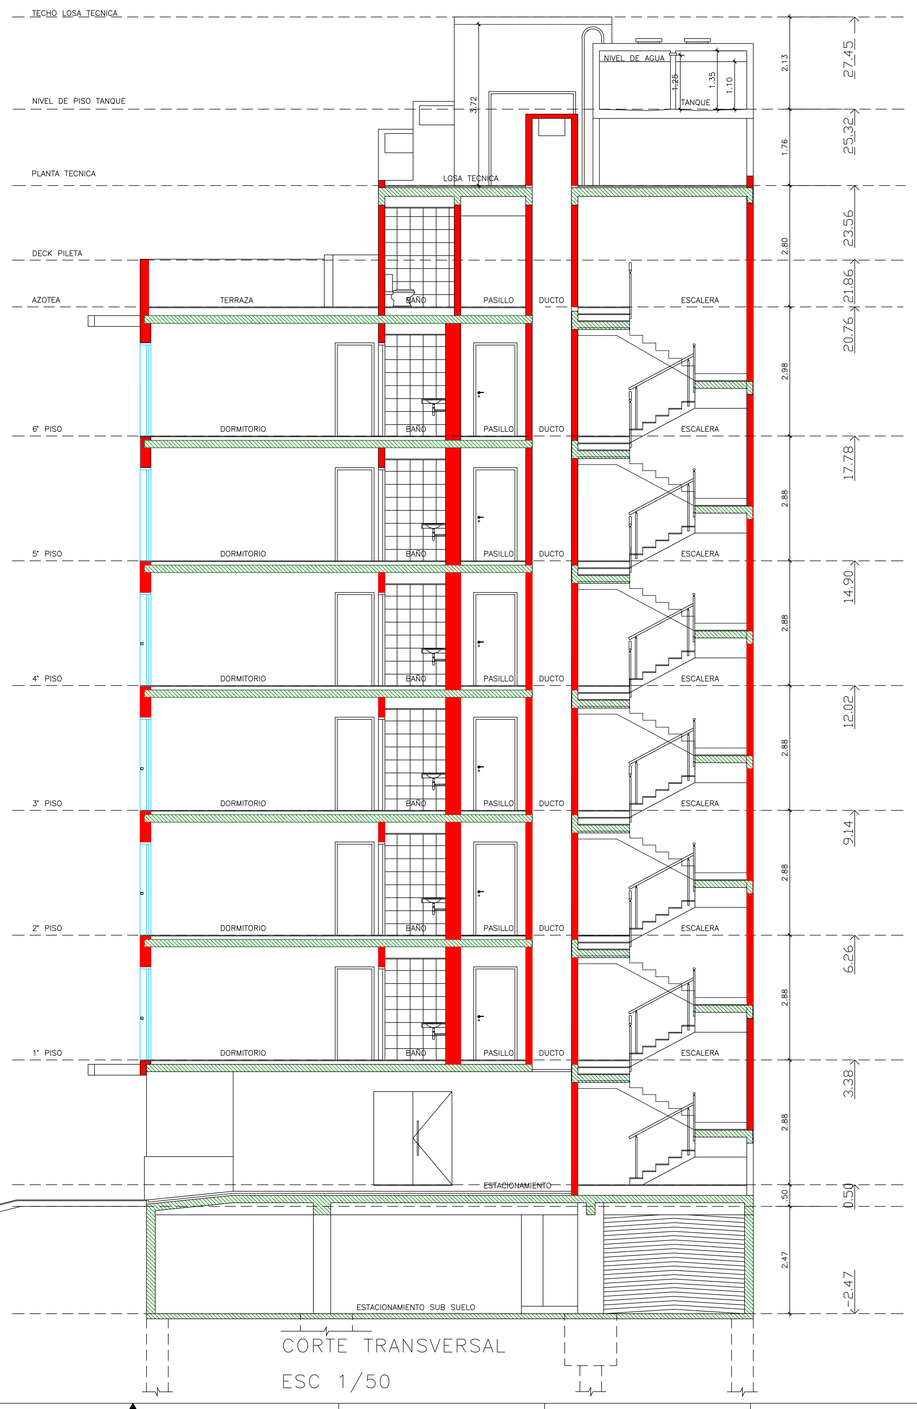


CORTE TRANSVERSAL
ESC 1/50

ARQ. FACHADA S/ 4 JULIO-CORTE TRANSVERSAL

OBRA: EDIF. DE DEPTOS.-VIV. MULTIFAMILIAR

LAMINA N°.

UBICACION: Concejal Vargas esq. 4 de Julio Cta.Cte.Ctral.N°:14-502-04

PROPIETARIO: CRISTINO SILVA

DOMICILIO: Gral. Garay c/ Laureles. Luque

PROFESIONAL PROYECTISTA: ARQ. MIGUEL ÁNGEL ALTIERI PAT.PROF.N°:2.473

DOMICILIO: Avda. Boggiani N°5832 c/RI 6 Boqueron

SUP. DEL TERRENO:469,00m2 SUP. TOTAL CONSTRUIDA.: 2.624m2

PROPIETARIO PROFESIONAL